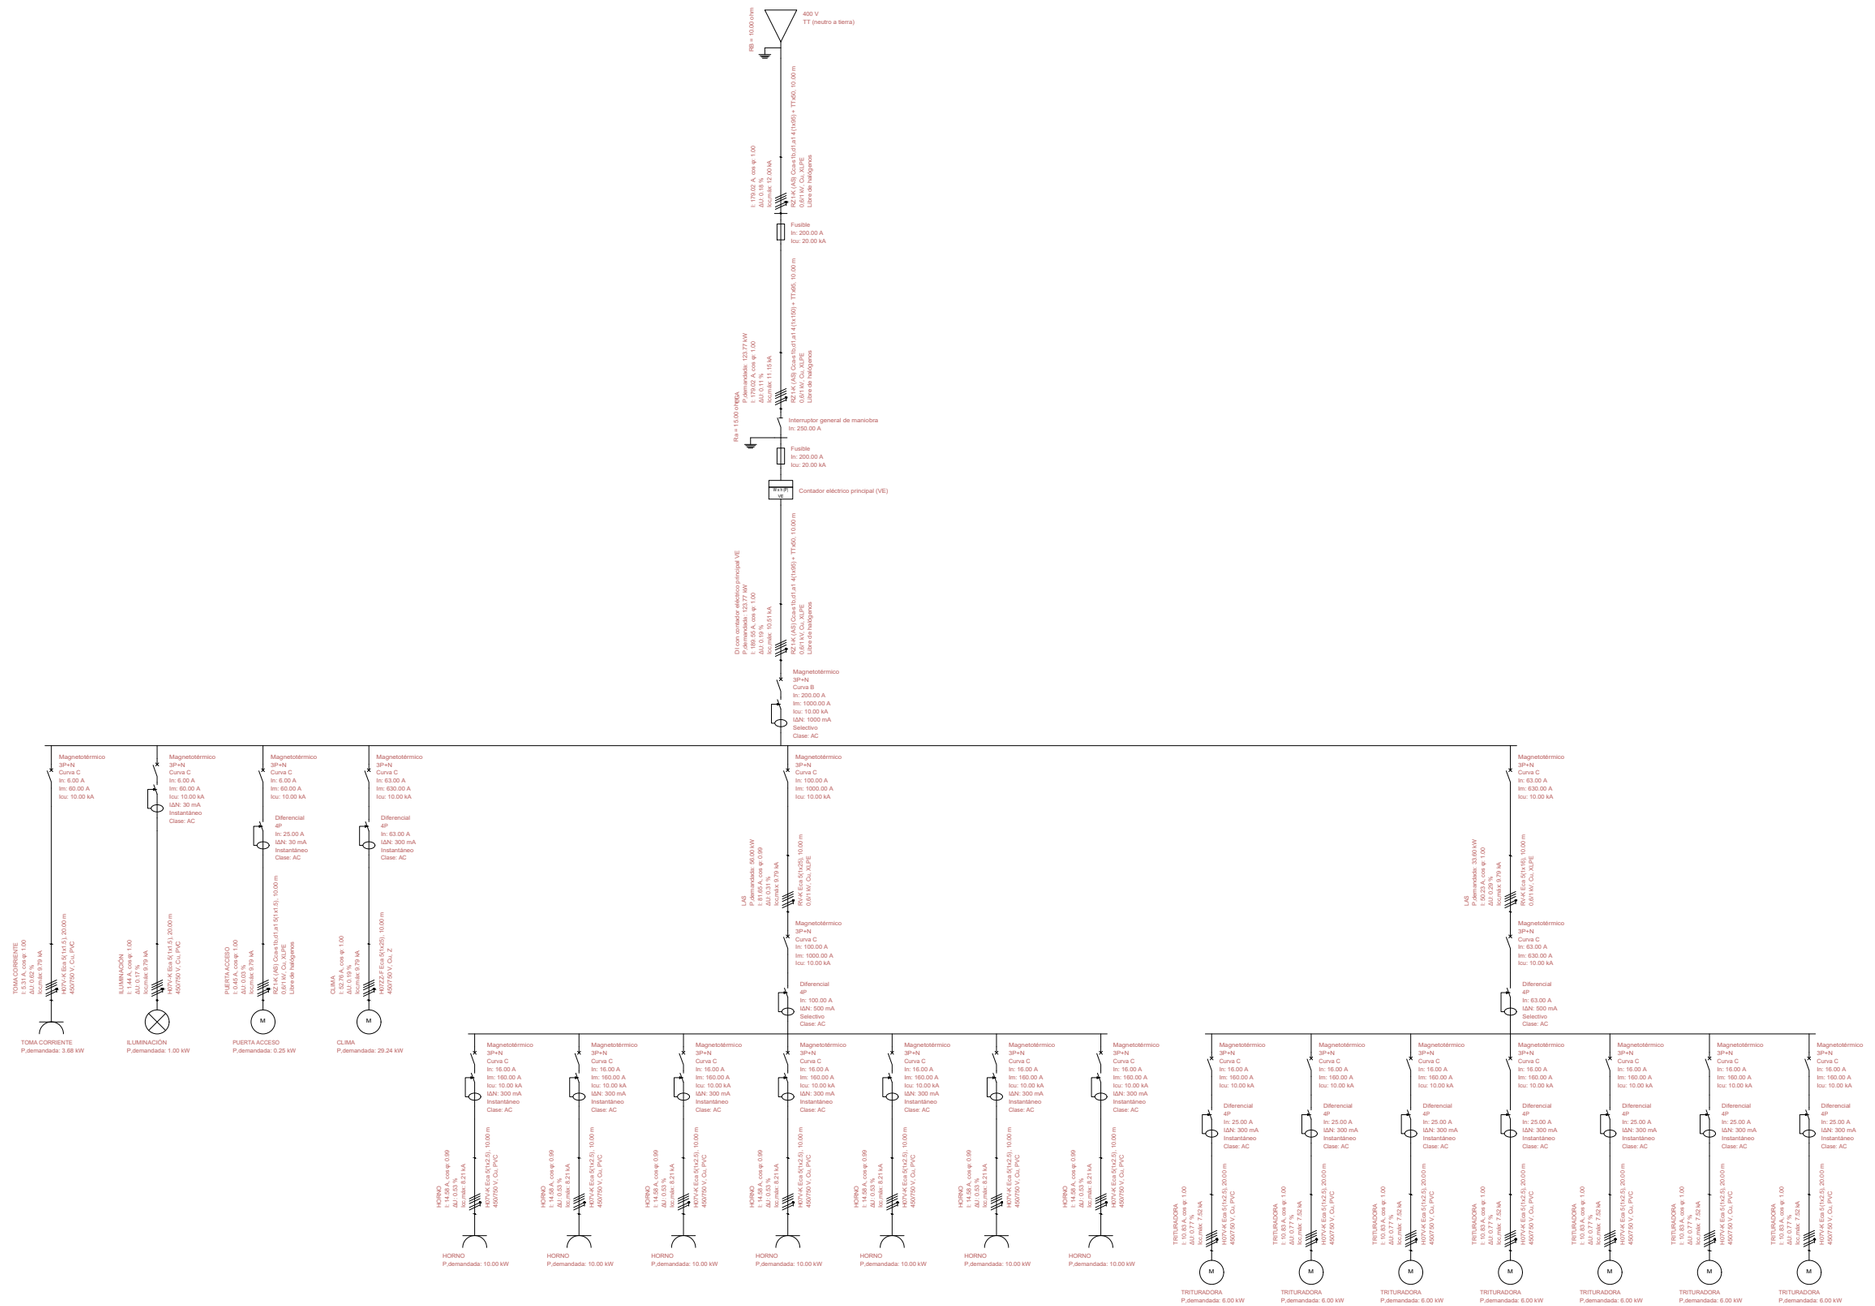


UNIVERSITAT POLITÈCNICA DE VALÈNCIA **EPS Alcoy** GRADO EN INGENIERÍA MECÁNICA AUTOR: Estudiante de la EPSA	TÍTULO: PROYECTO DE LA INSTALACIÓN ELÉCTRICA DE UNA NAVE INDUSTRIAL SITUADA EN COCENTAINA PLANO: PLANO UNIFILAR DE LA INSTALACIÓN ELÉCTRICA	FECHA: 12/11/2023 Escala: 8/1 Plano Número: 1