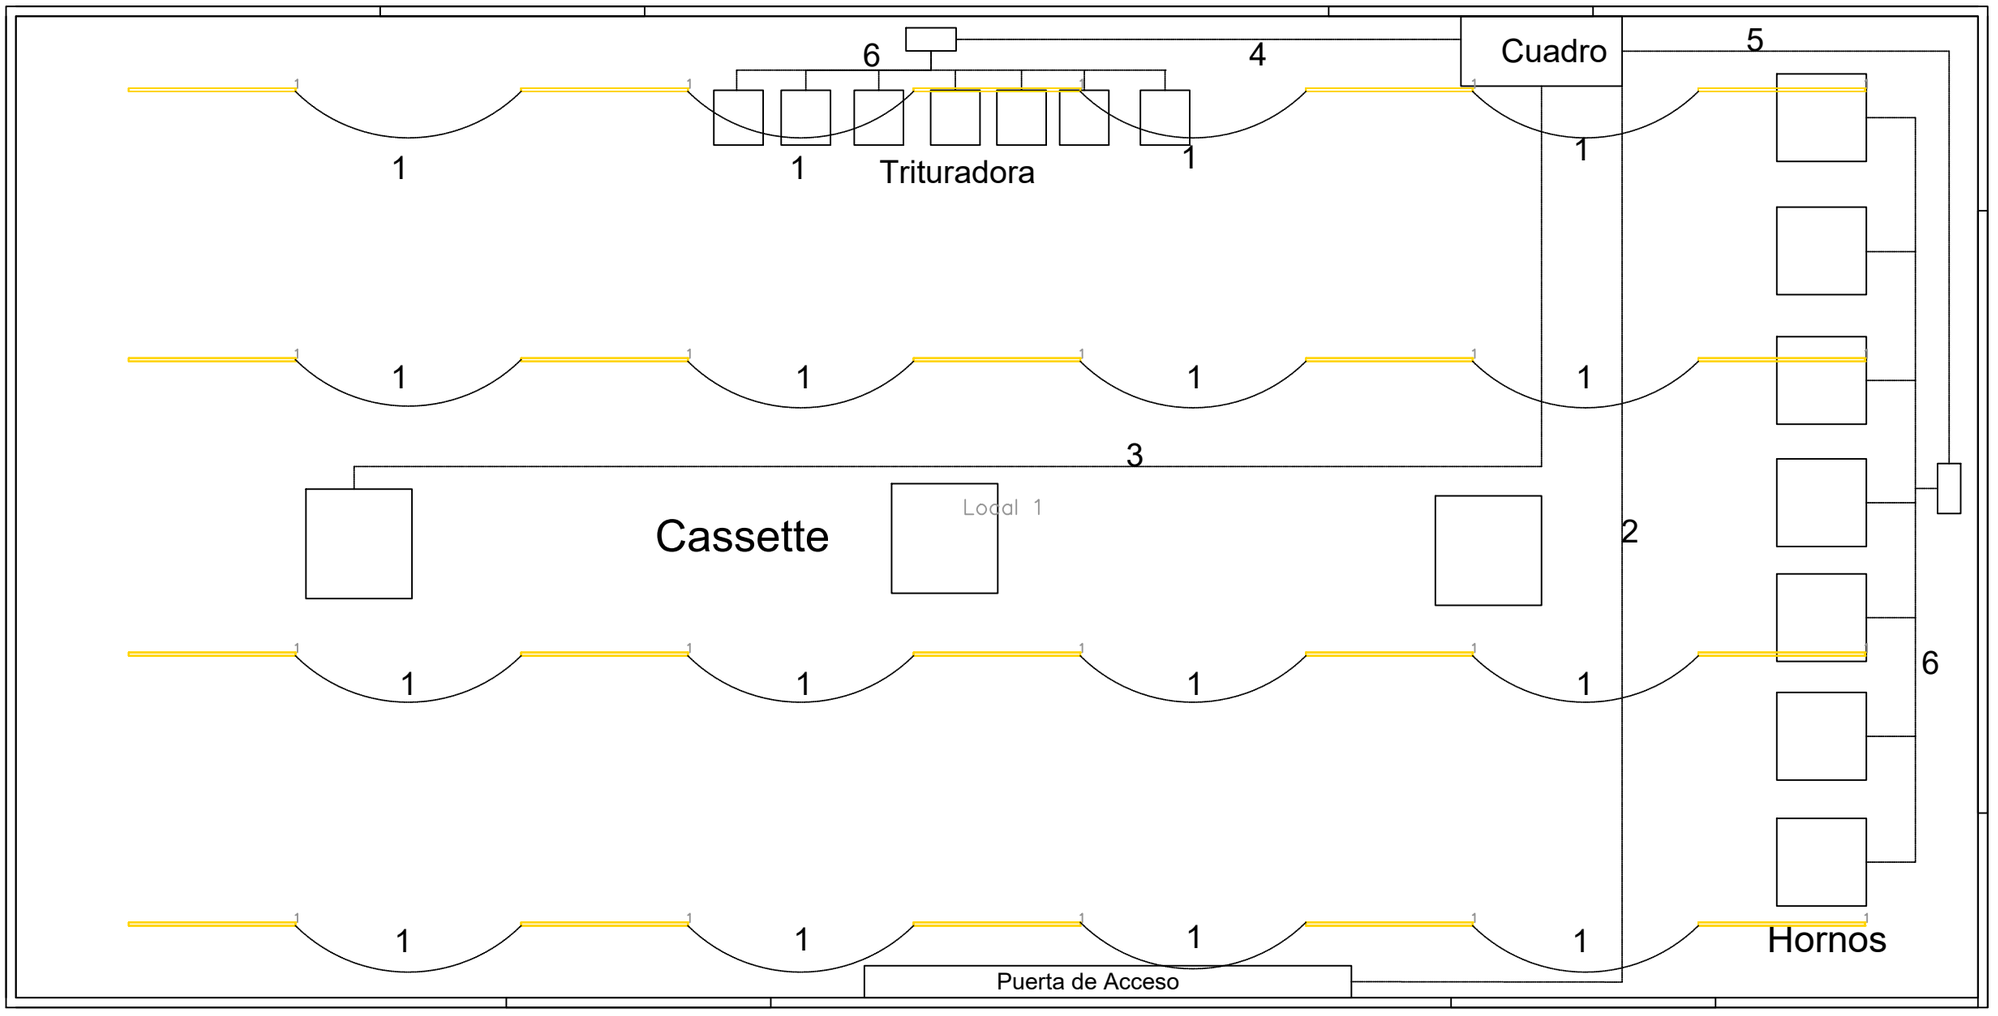


Cables	
1	H07V-K Eca 5(1x1.5)
2	RZ1-K (AS) Cca-s1b,d1,a1 5(1x1.5)
3	H07ZZ-F Eca 5(1x25)
4	RV-K Eca 5(1x16)
5	RV-K Eca 5(1x25)
6	H07V-K Eca 5(1x2.5)

UNIVERSITAT POLITÈCNICA DE VALÈNCIA

EPS Alcoy
GRADO EN INGENIERÍA MECÁNICA

AUTOR:
Estudiante de la EPSA

TÍTULO:
PROYECTO DE LA INSTALACIÓN ELÉCTRICA DE UNA NAVE INDUSTRIAL SITUADA EN COCENTAINA

PLANO:
PLANO DE DISTRIBUCIÓN DE LA INSTALACIÓN ELECTICA

FECHA: 12/11/2023

Escala: 8/1

Plano Número: 1