
EMPLAZAMIENTO · E 1:350

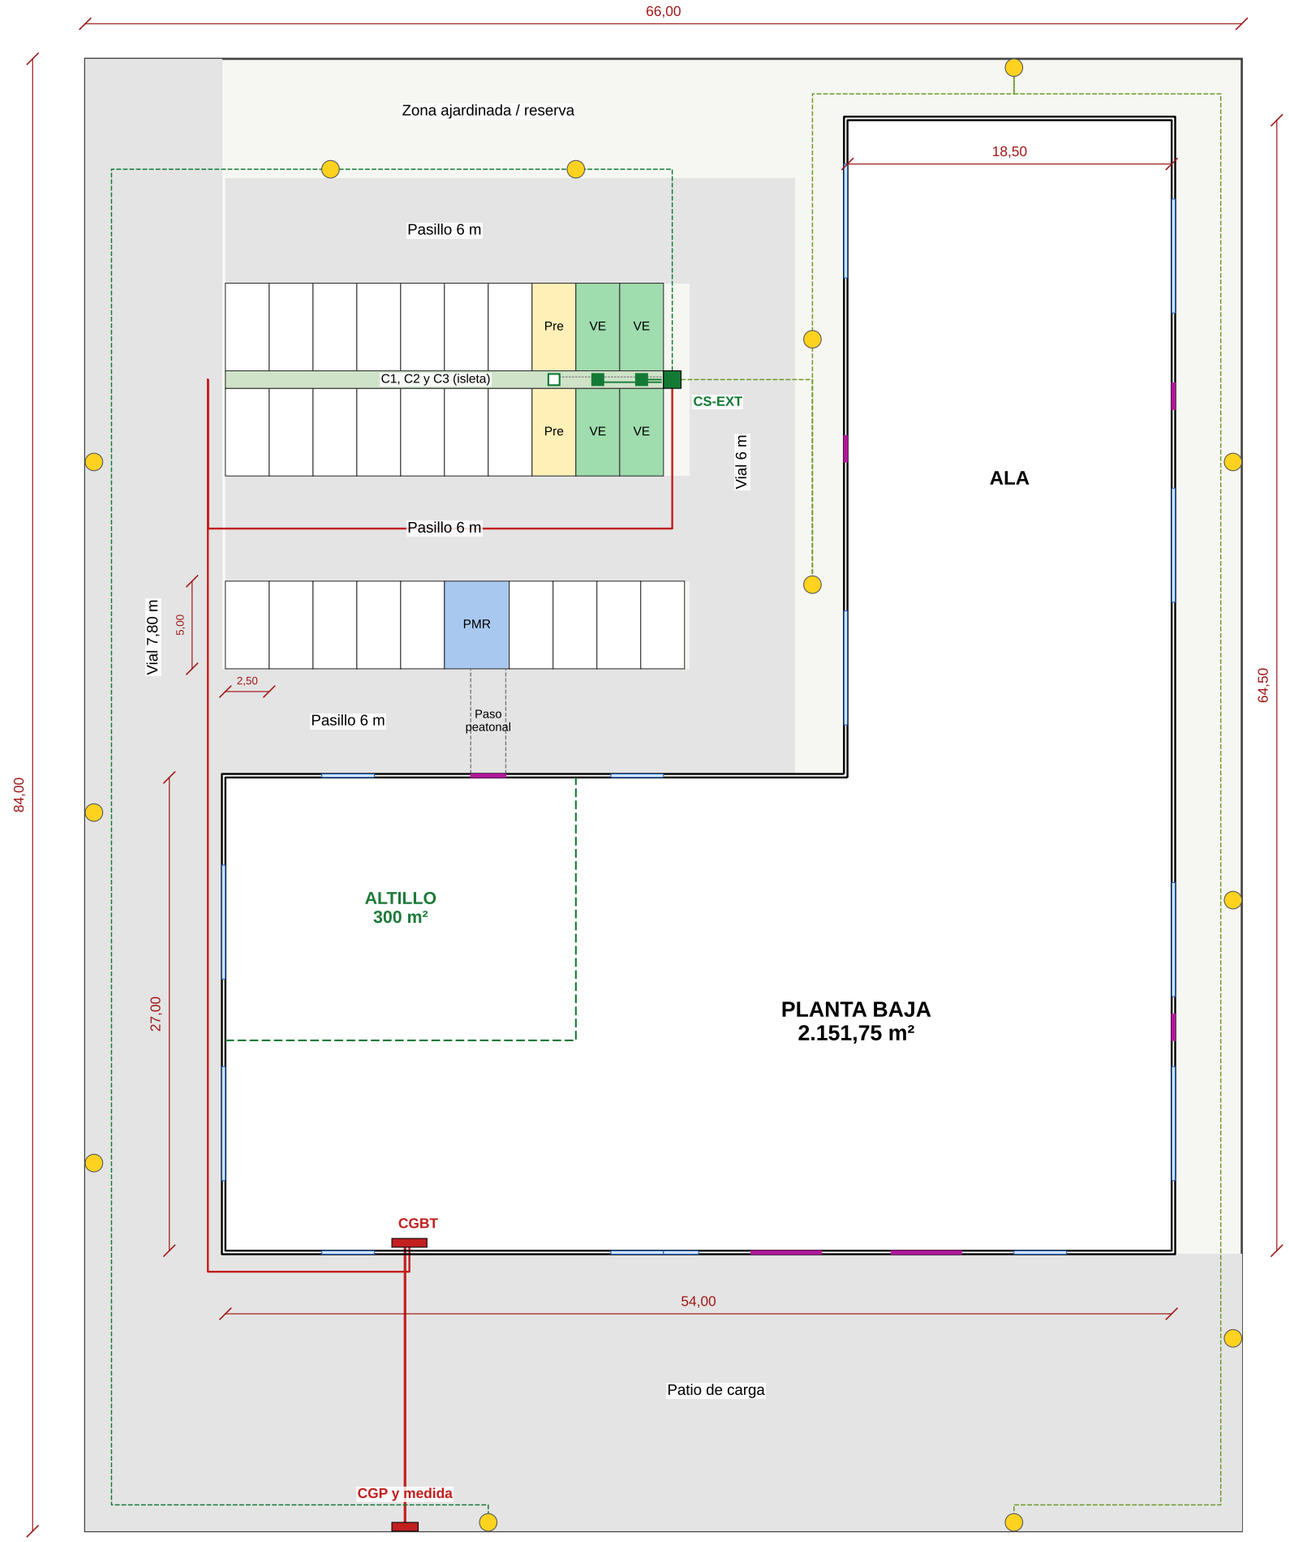

EXTERIORES

Concepto	Valor
Parcela	5.544 m²
Planta baja interior	2.151,75 m²
Altillo	300 m² (13,9 %)
Plazas de aparcamiento	30
Cargadores dobles instalados (C1 y C2)	2
Plazas con punto de recarga	4
Cargador doble previsto (C3)	1 (2 plazas)
Plazas con conducciones	6 (20 %)
Plaza accesible	1
Luminarias exteriores	13

LÍNEAS (PROPUESTA)

Línea	L en planta
Derivación individual: CGP y medida a CGBT	16 m
CGBT a CS-EXT	107 m
Recarga: CS-EXT a C1 / C2 (por salida)	1 / 4 m
Alumbrado exterior E1	142 m
Alumbrado exterior E2	166 m

LEYENDA

- Plaza con punto de recarga
- Plaza con cargador previsto
- Plaza accesible (PMR)
- Cargador doble instalado
- Cargador doble previsto
- Punto de luz exterior
- CGP, medida o cuadro
- Derivación y línea a CS-EXT (enterrada)
- Alumbrado exterior (enterrado)

Cotas en metros. Trazados y posición de luminarias: propuesta.
Se supone que la calle y la acometida están al sur del dibujo: falta el emplazamiento real y la orientación del norte.

UNIVERSITAT POLITÈCNICA DE VALÈNCIA

EPS Alcoy

GRADO EN INGENIERÍA MECÁNICA

AUTORES:
Ferran Bertomeu Peñarrocha
Álvaro Rubio Ordoñez
Néstor Ordiñana Fenollar

TÍTULO:

PROYECTO DE LA INSTALACIÓN ELÉCTRICA DE BAJA TENSIÓN DE UNA PANADERÍA INDUSTRIAL

PLANO:

PLANO DE EMPLAZAMIENTO

FECHA: 13/11/2026


ESCALA: 1:350

PLANO Nº: **1**

DISTRIBUCIÓN DE LA INSTALACIÓN

PLANTA ALTILLO (300 m²) · E 1:150

PLANTA BAJA (2.151,75 m²) · E 1:250

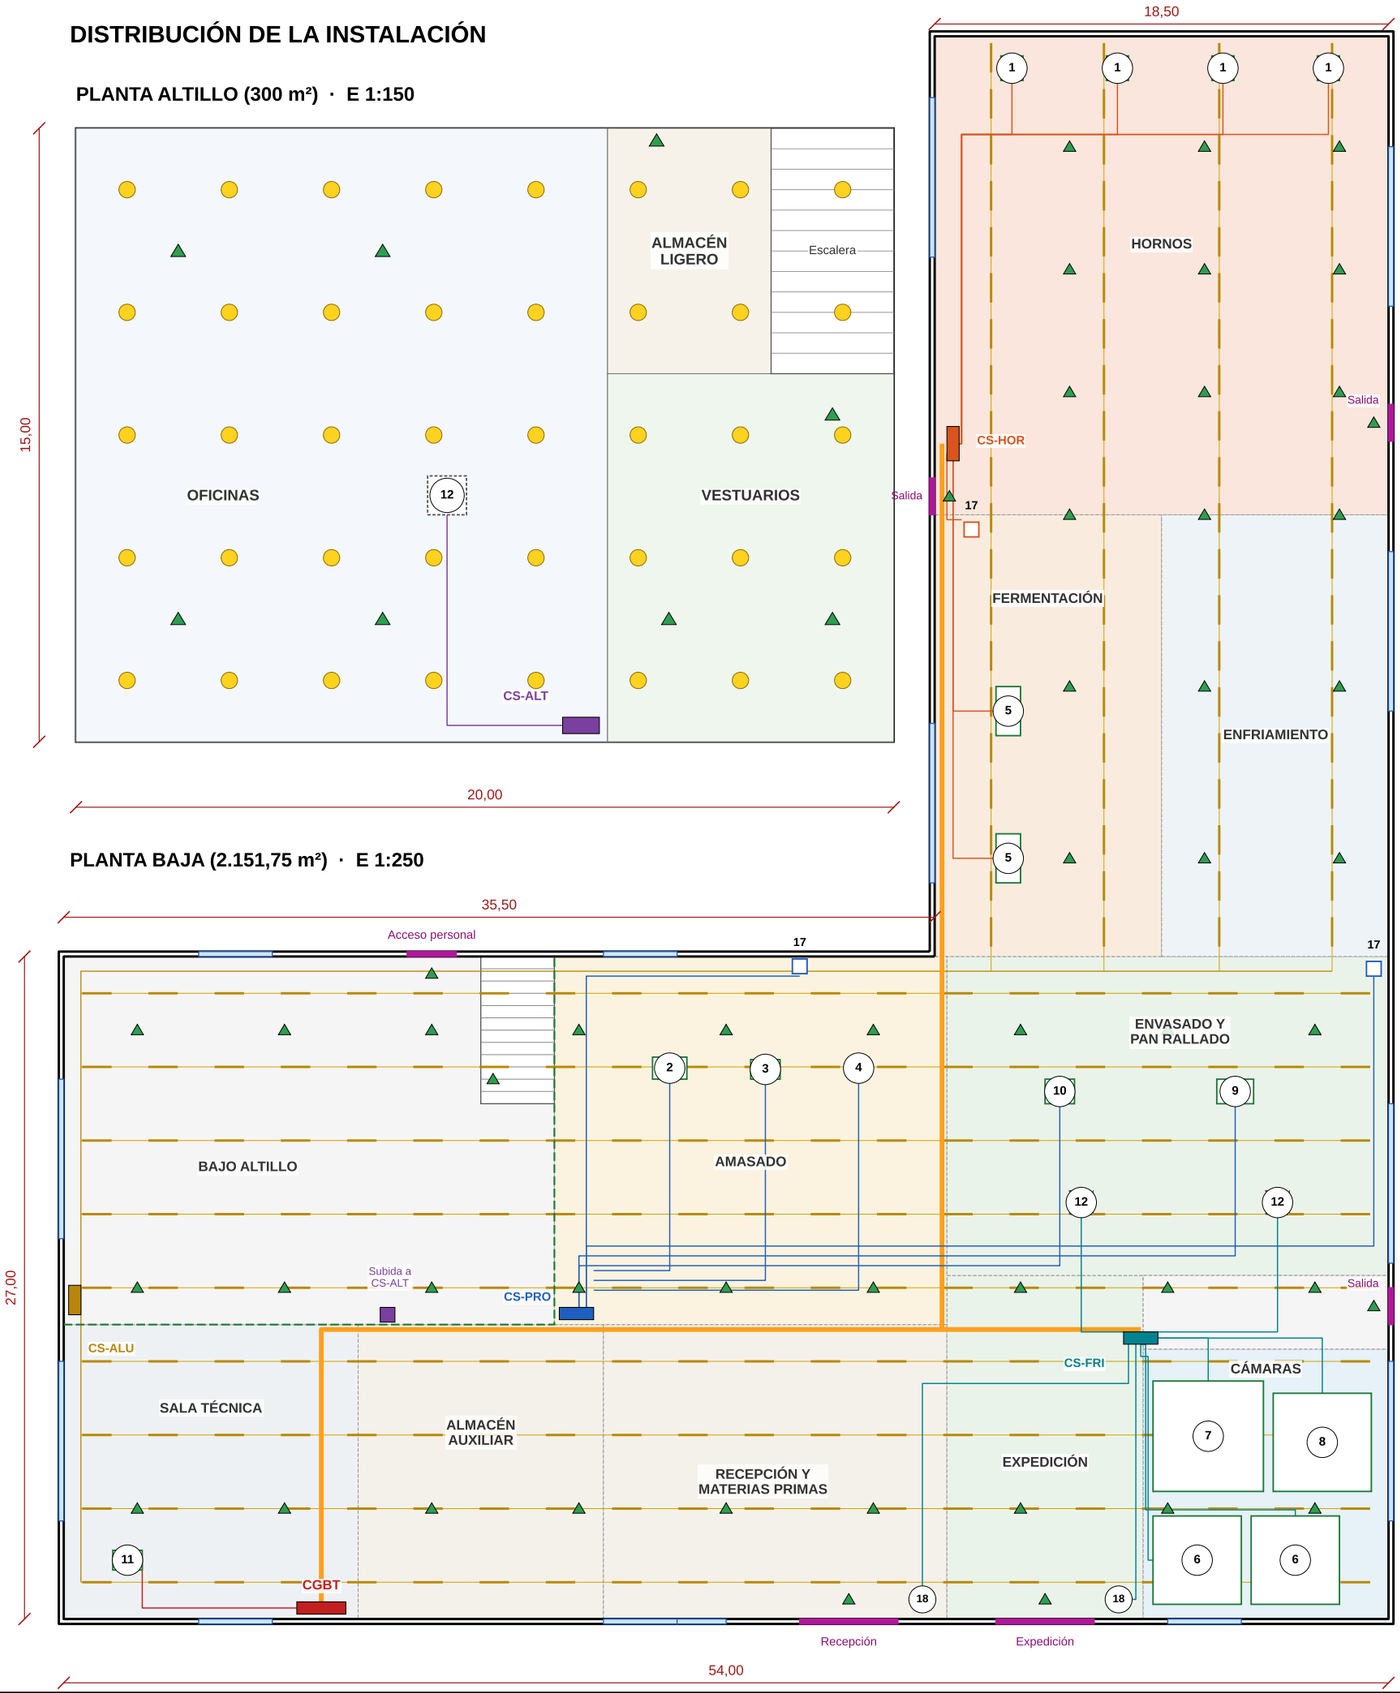

RECEPTORES

Nº	Receptor	Modelo	Uds	P (kW)	Cuadro	L (m)
1	Horno de convección	Unox XEFT-06EU-EMRV	4	41,20	CS-HOR	30
2	Amasadora espiral 130 kg	Bongard Spiral EVO 200	1	6,80	CS-PRO	11
3	Amasadora espiral 80 kg	Bongard Spiral EVO 110	1	4,55	CS-PRO	15
4	Batidora planetaria 60 L	Bongard Saturne EVO 60	1	3,10	CS-PRO	19
5	Cámara de fermentación	Sveba Dahlen F500 HIK	2	8,00	CS-HOR	19
6	Congelación -20 °C, 32 m³	Intarcon BCV-NG-3 096	2	4,78	CS-FRI	13
7	Conservación 0 °C, 51 m³	Intarcon MCV-NY-3 108	1	2,48	CS-FRI	4
8	Conservación 0 °C, 40 m³	Intarcon MCV-NY-3 074	1	1,89	CS-FRI	9
9	Ensacadora	Por definir	1	5,50	CS-PRO	35
10	Trituradora de pan	Por definir	1	6,00	CS-PRO	28
11	Compresor de tornillo	Atlas Copco GA 5	1	6,14	CGBT	8
12	Cassette climatización	Mitsubishi PLA-RP140BA	3	15,63	CS-FRI/ALT	10
13	Alumbrado producción	Philips WT120C LED40S/840	260	10,66	CS-ALU	101
14	Alumbrado altillo	Philips DN065B LED20S/830	40	0,92	CS-ALT	—
15	Alumbrado exterior	Philips BRP102 LED74/740	13	0,61	CS-EXT	Pl. 2
16	Alumbrado emergencia	Legrand URA21 660611PL	60	0,14	CS-ALU/ALT	—
17	Línea de tomas 16 A	Schneider PKF16G423	3	11,04	CS-PRO/HOR	46
18	Puerta de muelle	Hörmann WA300R S4/SE	2	0,50	CS-FRI	19
19	Punto de recarga 32 A	Schneider EVB3S07N4A	4	29,60	CS-EXT	Pl. 2
	POTENCIA NOMINAL TOTAL			**159,54**		

CUADROS (PROPUESTA)

Cuadro	Alimenta	L desde CGBT (m)
CGBT	Cuadro general de baja tensión	—
CS-PRO	Amasado, envasado y tomas	22
CS-HOR	Hornos, fermentación y tomas	73
CS-FRI	Cámaras, puertas y climatización	44
CS-ALU	Alumbrado y emergencia de nave	22
CS-ALT	Altillo (alumbrado, climatización)	14
CS-EXT	Recarga y alumbrado exterior	Pl. 2

LEYENDA

- Luminaria estanca (13 líneas de 20)
- Luminaria de emergencia
- Downlight altillo
- Bandeja principal
- Circuito (color del cuadro)
- Máquina (nº de la tabla)
- Cassette en techo
- Puerta
- Ventana
- Límite del altillo sobre planta baja

Cotas en metros. Ubicación de máquinas, cuadros y trazados: propuesta.
Dimensiones de máquinas orientativas. Alumbrado provisional hasta cerrar DIALux.
L: longitud en planta del circuito más largo, sin subidas ni bajadas a equipos.

UNIVERSITAT POLITÈCNICA DE VALÈNCIA

EPS Alcoy

GRADO EN INGENIERÍA MECÁNICA

AUTORES:
Ferran Bertomeu Peñarrocha
Álvaro Rubio Ordoñez
Néstor Ordiñana Fenollar

TÍTULO:

PROYECTO DE LA INSTALACIÓN ELÉCTRICA DE BAJA TENSIÓN DE UNA PANADERÍA INDUSTRIAL

PLANO:

PLANO DE DISTRIBUCIÓN DE LA INSTALACIÓN
PLANTA BAJA Y ALTILLO

FECHA: 13/11/2026

ESCALA: 1:250 / 1:150

PLANO Nº: **2**