
EMPLAZAMIENTO · E 1:400

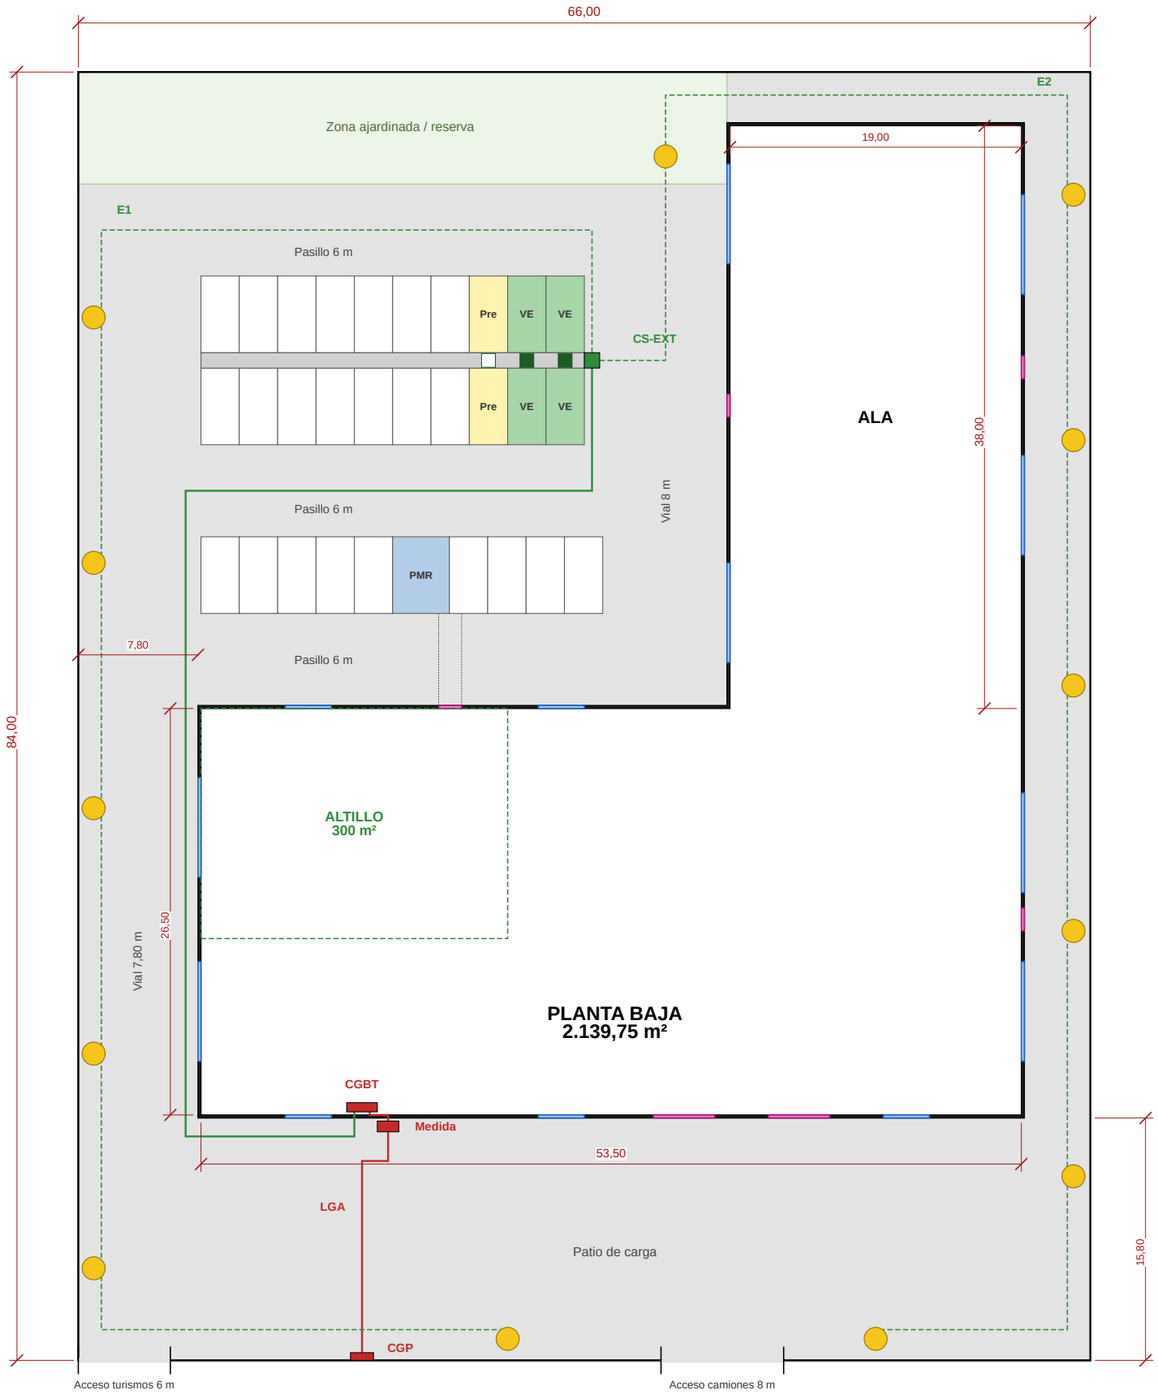

EXTERIORES

Concepto	Valor
Parcela (66 × 84 m)	5.544 m²
Planta baja interior	2.139,75 m²
Altillo (20,00 × 15,00 m)	300 m² (14,0 % de la planta baja)
Plazas de aparcamiento (2,50 × 5,00 m)	30
Cargadores dobles instalados (C1 y C2)	2
Plazas con punto de recarga	4
Cargador doble previsto (C3)	1 (2 plazas)
Plazas con conducciones	6 (20 %)
Plaza accesible	1
Luminarias exteriores	13

LÍNEAS (PROPUESTA)

Línea	L en planta
LGA: CGP a equipo de medida	16 m
Derivación individual: medida a CGBT	1,8 m
CGBT a CS-EXT	89 m
Alumbrado exterior E1	138 m
Alumbrado exterior E2	141 m

LEYENDA

- Plaza con punto de recarga
- Plaza con cargador previsto
- Plaza accesible (PMR)
- Cargador doble instalado
- Cargador doble previsto
- Punto de luz exterior
- CGP, medida o cuadro
- LGA y derivación individual
- Línea CGBT a CS-EXT
- Alumbrado exterior (enterrado)
- Zona ajardinada

Cotas en metros. Trazados y posición de luminarias: propuesta.
Se supone que la calle y la acometida están al sur del dibujo; falta el emplazamiento real y la orientación del norte.

UNIVERSITAT POLITÈCNICA DE VALÈNCIA

EPS Alcoy

GRADO EN INGENIERÍA MECÁNICA

AUTORES:
Ferran Bertomeu Peñarrocha
Álvaro Rubio Ordoñez
Néstor Ordiñana Fenollar

TÍTULO:
PROYECTO DE LA INSTALACIÓN ELÉCTRICA DE BAJA TENSIÓN DE UNA PANADERÍA INDUSTRIAL

PLANO:
PLANO DE EMPLAZAMIENTO

FECHA:
12/11/2026


ESCALA:
1:400

PLANO Nº:
1

DISTRIBUCIÓN DE LA INSTALACIÓN

PLANTA ALTILLO (300 m²) · E 1:200

PLANTA BAJA (2.139,75 m²) · E 1:300

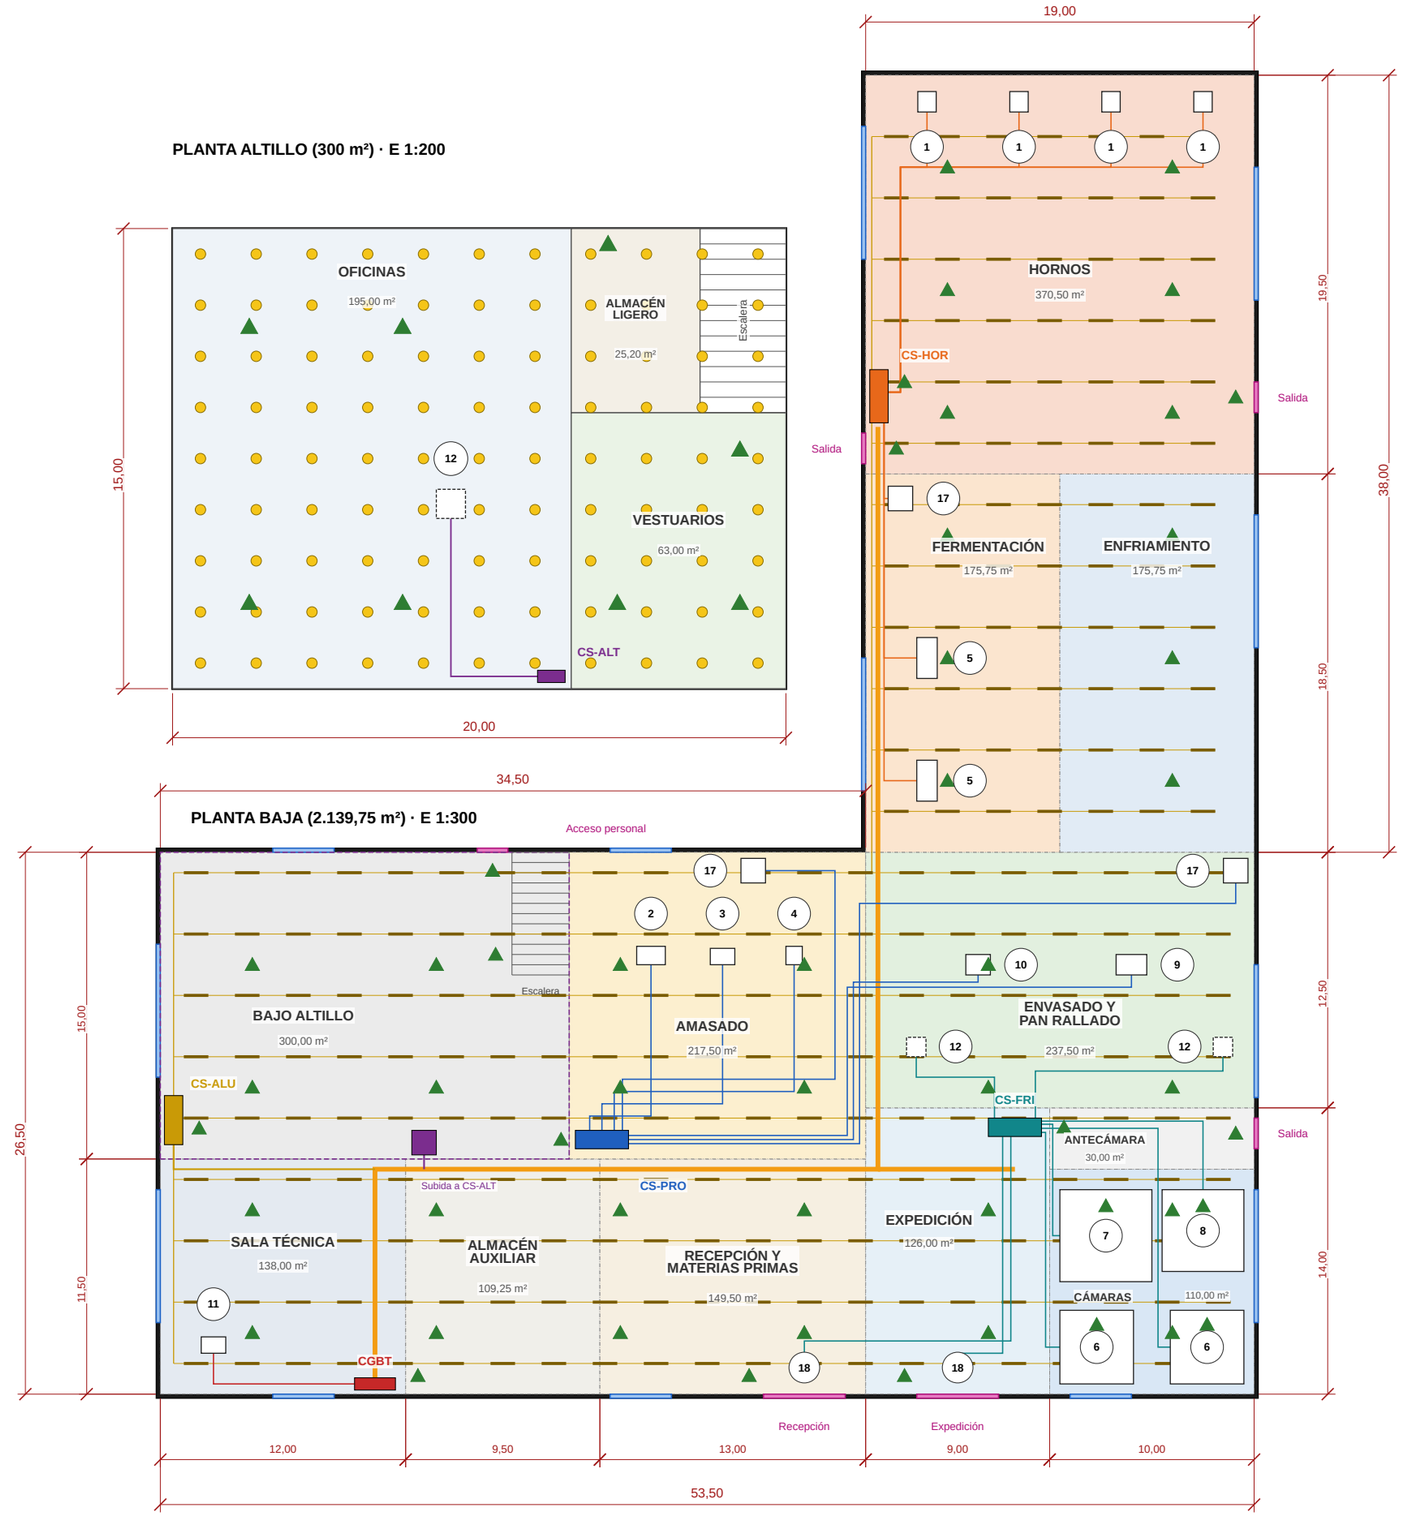

RECEPTORES

Nº	Receptor	Modelo	Uds	P (kW)	Cuadro	L (m)
1	Horno de convección	Unox XEFT-06EU-EMRV	4	41,20	CS-HOR	30
2	Amasadora espiral 130 kg	Bongard Spiral EVO 200	1	6,80	CS-PRO	12
3	Amasadora espiral 80 kg	Bongard Spiral EVO 110	1	4,55	CS-PRO	14
4	Batidora planetaria 60 L	Bongard Saturne EVO 60	1	3,10	CS-PRO	17
5	Cámara de fermentación	Sveba Dahlen F500 HIK	2	8,00	CS-HOR	20
6	Congelación −20 °C, 32 m³	Intarcon BCV-NG-3 096	2	4,78	CS-FRI	17
7	Conservación 0 °C, 51 m³	Intarcon MCV-NY-3 108	1	2,48	CS-FRI	7
8	Conservación 0 °C, 40 m³	Intarcon MCV-NY-3 074	1	1,89	CS-FRI	12
9	Ensacadora	Por definir	1	5,50	CS-PRO	33
10	Trituradora de pan	Por definir	1	6,00	CS-PRO	26
11	Compresor de tornillo	Atlas Copco GA 5	1	6,14	CGBT	9
12	Cassette climatización	Mitsubishi PLA-RP140BA	3	15,63	CS-FRI/ALT	13
13	Alumbrado producción	Philips WT120C LED40S/840	328*	39,69	CS-ALU	98
14	Alumbrado altillo	Philips DN065B LED20S/830	99	1,88	CS-ALT	—
15	Alumbrado exterior	Philips BRP102 LED74/740	13	0,61	CS-EXT	Pl. 1
16	Alumbrado emergencia	Legrand URA21 660611PL	60	0,14	CS-ALU/ALT	—
17	Línea de tomas 16 A	Schneider PKF16G423	3	11,04	CS-PRO/HOR	43
18	Puerta de muelle	Hörmann WA300R S4/SE	2	0,50	CS-FRI	21
19	Punto de recarga 32 A	Schneider EVB3S07N4A	4	29,60	CS-EXT	Pl. 1
	POTENCIA NOMINAL TOTAL			**189,53**		

CUADROS (PROPUESTA)

Cuadro	Alimenta	L desde CGBT (m)
CGBT	Cuadro general de baja tensión	—
CS-PRO	Amasado, envasado y tomas	23
CS-HOR	Hornos, fermentación y tomas	72
CS-FRI	Cámaras, puertas y climatización	44
CS-ALU	Alumbrado y emergencia de nave	22
CS-ALT	Altillo (alumbrado, climatización)	14 + subida
CS-EXT	Recarga y alumbrado exterior	Pl. 1

LEYENDA

- Luminaria estanca (9+12 líneas, 273 uds)
- Luminaria de emergencia (60 uds)
- Downlight altillo (99 uds, DIALux)
- Bandeja principal
- Circuito (color del cuadro)
- (n) Receptor nº n de la tabla
- Máquina o equipo
- Cassette en techo
- Puerta
- Ventana
- Límite del altillo sobre planta baja

Cotas en metros. Ubicación de máquinas, cuadros y trazados: propuesta.

* Alumbrado de planta baja provisional: 273 luminarias dibujadas frente a 328 de la tabla de receptores; ambas se cierran con el DIALux de la nave nueva.

L: longitud en planta del circuito más largo, sin subidas ni bajadas a equipos.

UNIVERSITAT POLITÈCNICA DE VALÈNCIA

EPS Alcoy

GRADO EN INGENIERÍA MECÁNICA

AUTORES:

Ferran Bertomeu Peñarrocha

Álvaro Rubio Ordoñez

Néstor Ordiñana Fenollar

TÍTULO:

PROYECTO DE LA INSTALACIÓN ELÉCTRICA DE BAJA TENSIÓN DE UNA PANADERÍA INDUSTRIAL

PLANO:

PLANO DE DISTRIBUCIÓN DE LA INSTALACIÓN PLANTA BAJA Y ALTILLO

FECHA: 12/11/2026

ESCALA: 1:300 / 1:200

PLANO Nº: **2**